
Отопление. Расчетное кольцо через Р105

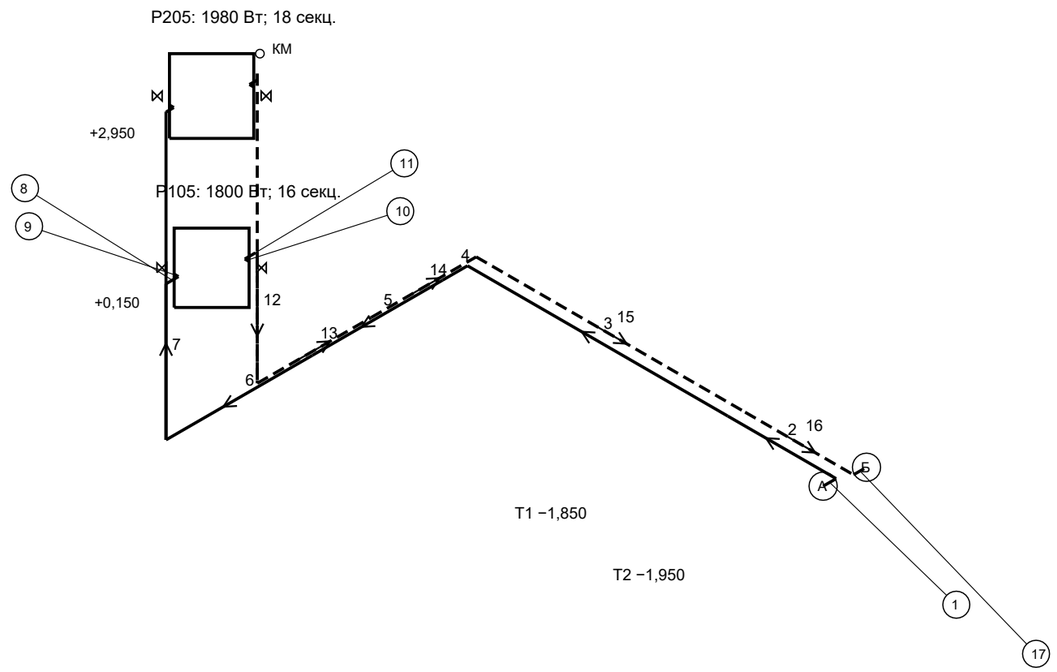

№	Qуч, кВт	G, кг/ч	L, м	DN
1	30.47	1051	0.30	25
2	17.64	608	2.50	20
3	15.24	525	6.00	20
4	8.82	304	0.57	20
5	6.42	221	3.00	20
6	4.01	138	3.38	20
7	4.01	138	2.54	15
8	1.91	66	0.29	15
9	1.91	66	0.10	15
10	1.91	66	0.10	15
11	1.91	66	0.29	15
12	4.01	138	2.14	15
13	4.01	138	2.62	20
14	6.42	221	2.43	20
15	15.24	525	6.20	20
16	17.64	608	2.50	20
17	30.47	1051	0.30	25

Участки 1–9 — Т1; 10–17 — Т2.

Тепловой узел соединяется с кольцом в точках А, Б.

Остальные стояки — ответвления от магистралей.


Ст.ЛК: отдельная проточная ветвь с одним прибором.

ΣL = 35.26 м; потери кольца 5770 Па.

БК: ΔP = 2866 Па; Kv = 6.27.

КМ — кран Маевского; арматура отсечения и слива у оснований стояков.

Тепловой узел (б/м)

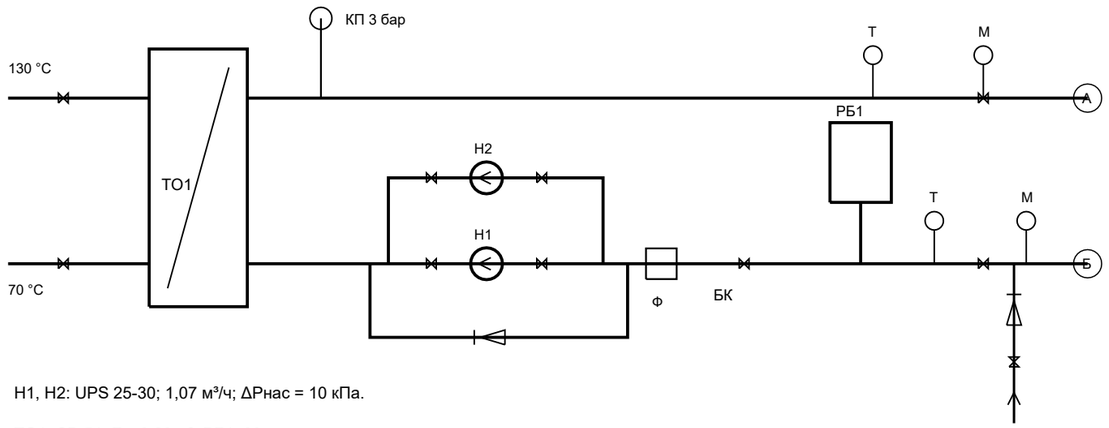

Н1, Н2: UPS 25-30; 1,07 м³/ч; ΔРнас = 10 кПа.

ТО1: СВ-51, F ≥ 0,20 м²; РБ1: 80 л.

Подпитка от водопровода

Подбор узла — по расчетным условиям пособия.

М 1:100

ОВ-178. Отопление и вентиляция здания

Отопление. Расчетное кольцо через Р105

Жилой дом. Комсомольск-на-Амуре

	Фамилия	Подпись	Дата
Разраб.	_____		
Проверил	_____		

Стадия У | Лист 4 | Листов 5