
План 1 этаж. Отопление и вентиляция

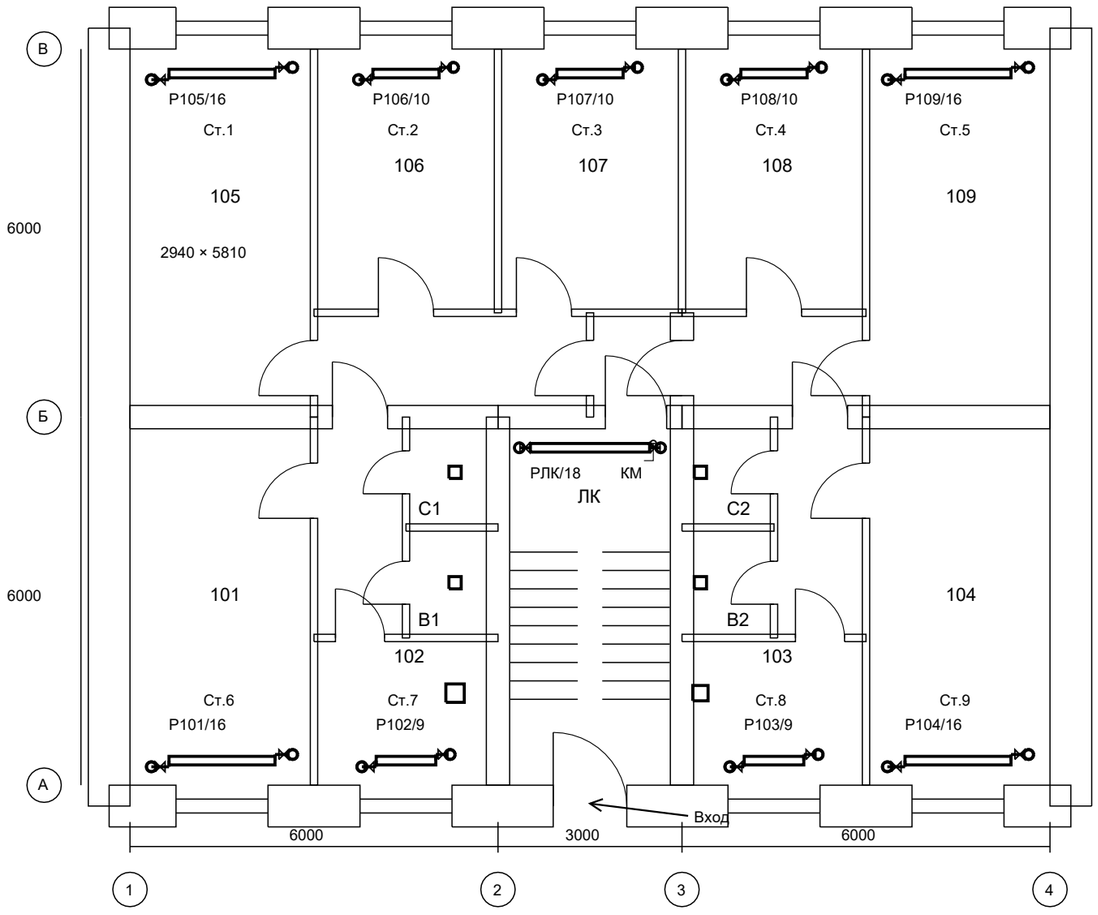

Фасад А–А — географический запад

Размеры окон 1500×1400 мм, высота подоконника 900 мм.

Привязки перегородок и открывание дверей — по плану.

Приборы: высота 588 мм, низ +0,150 м от пола.

№	Помещение	Площадь*, м²
101	Жилая	17,08
102	Кухня	6,43
103	Кухня	6,43
104	Жилая	17,08
105	Жилая	17,08
106	Жилая	12,21
107	Жилая	12,21
108	Жилая	12,21
109	Жилая	17,08
ЛК	Лестница	15,22
В1	Ванная	2,10
С1	Туалет	1,94
В2	Ванная	2,10
С2	Туалет	1,94

* Площади помещений по плану;

ЛК — площадь в плане. Холлы и коридоры

не включены в жилую площадь квартир.

Т1 — подача 85 °С; Т2 — обратка 60 °С.

Стояки и подводки DN15. Р105/16 — прибор/секции.

КМ — кран Маевского; краны — по символам.

К1: 126 м³/ч, 300×300; К2: 90 м³/ч, 250×250.

В1, В2, С1, С2: по 25 м³/ч, 200×200 мм.

Вытяжка — отдельными каналами каждого этажа.

Приток — через неплотности ограждений.

М 1:100

ОВ-178. Отопление и вентиляция здания

План 1 этаж. Отопление и вентиляция

Жилой дом. Комсомольск-на-Амуре

	Фамилия	Подпись	Дата			
Разраб.	_____			Стадия У	Лист 2	Листов 5
Проверил	_____					