План подвала. Отопление

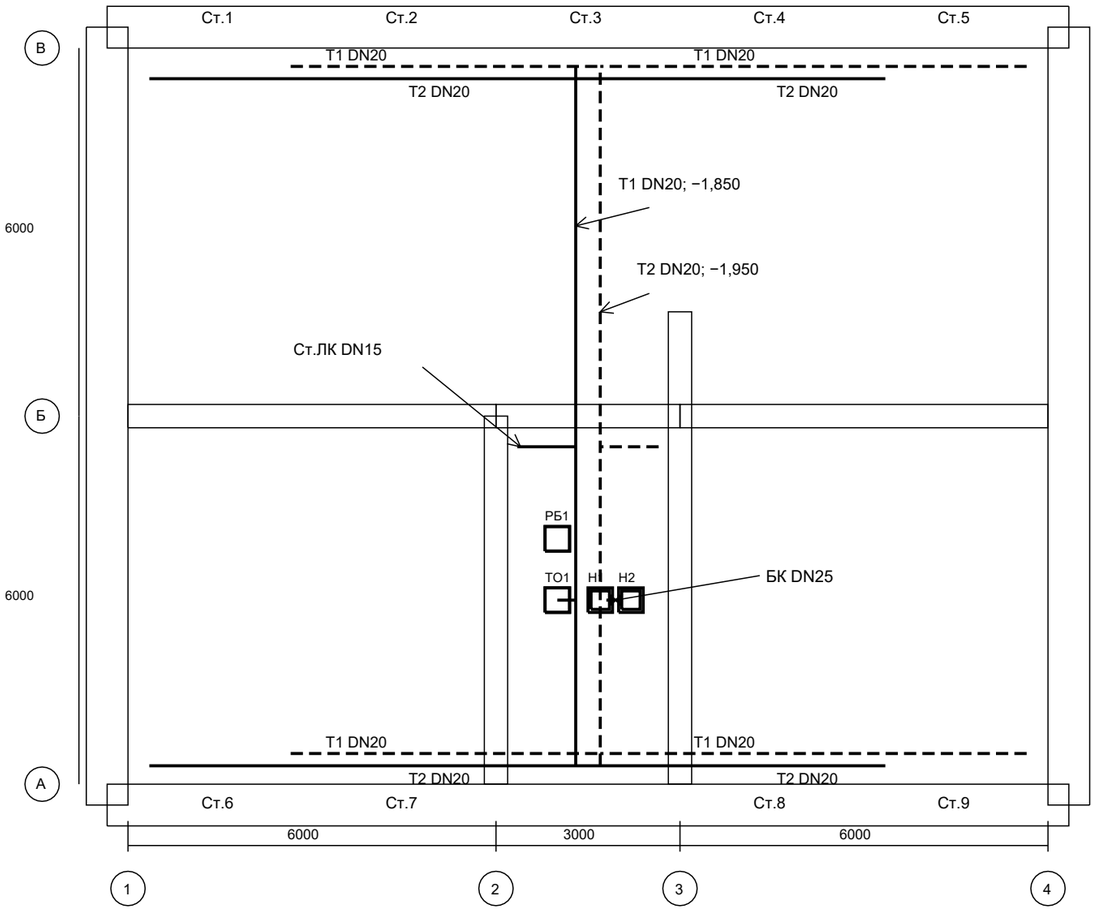

Фасад А–А — географический запад

Поз.	Оборудование	Количество
ТО1	Теплообменник СВ-51	1
Н1, Н2	Насос UPS 25-30	2
РБ1	Мембранный бак 80 л	1
БК	Клапан настройки Kv=6.27	1

От теплообменника до разветвления — DN25.

Главные и фасадные ветви — DN20.

Стояки 1–9 и отдельная ветвь ЛК — DN15.

На основаниях стояков — отсечки и слив.

Горизонтальные трубы теплоизолировать.

Уклон 0,003 к точкам опорожнения.

Уклон и монтажные узлы показаны схематично.

Габариты оборудования приняты для компоновки.

T1 — сплошная линия; T2 — штриховая.

Пол подвала −2,650; потолок −0,650 м.

Тепловой узел и расчетный стояк — лист ОВ-4.

М 1:100

ОВ-178. Отопление и вентиляция здания

План подвала. Отопление

Жилой дом. Комсомольск-на-Амуре

	Фамилия	Подпись	Дата
Разраб.	_____		
Проверил	_____		

Стадия У | Лист 1 | Листов 5