
# План 1 этаж. Отопление и вентиляция

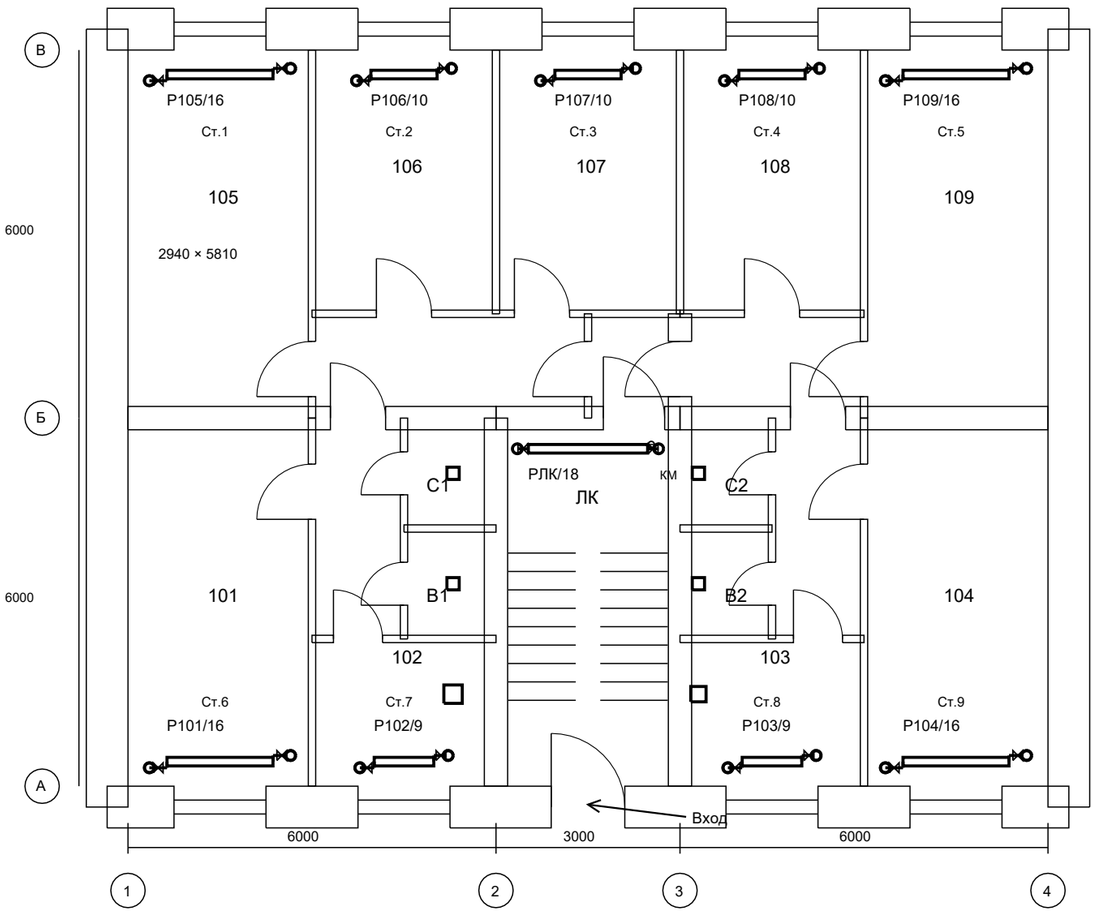


Фасад А–А — географический запад

| № | Помещение | Площадь*, м² |
|---|---|---|
| 101 | Жилая | 17,08 |
| 102 | Кухня | 6,43 |
| 103 | Кухня | 6,43 |
| 104 | Жилая | 17,08 |
| 105 | Жилая | 17,08 |
| 106 | Жилая | 12,21 |
| 107 | Жилая | 12,21 |
| 108 | Жилая | 12,21 |
| 109 | Жилая | 17,08 |
| ЛК | Лестница | 15,22 |
| В1 | Ванная | 2,10 |
| С1 | Туалет | 1,94 |
| В2 | Ванная | 2,10 |
| С2 | Туалет | 1,94 |

* Площади по принятой планировке;

ЛК — площадь в плане. Холлы и коридоры

не включены в жилую площадь квартир.

Т1 — подача 85 °С; Т2 — обратка 60 °С.

Стояки и подводки DN15. Р105/16 — прибор/секции.

КМ — кран Маевского; краны — по символам.

К1: 126 м³/ч, 300×300; К2: 90 м³/ч, 250×250.

В1, В2, С1, С2: по 25 м³/ч, 200×200 мм.

Вытяжка — отдельными каналами каждого этажа.

Приток через неплотности принят по пособию.

Размеры окон 1500×1400 мм, высота подоконника 900 мм.

Привязки перегородок и открывание дверей приняты по схеме.

Приборы: высота 588 мм, низ +0,150 м от пола.

М 1:100

ОВ-178. Отопление и вентиляция здания

План 1 этаж. Отопление и вентиляция

Жилой дом. Комсомольск-на-Амуре

| | Фамилия | Подпись | Дата |
|---|---|---|---|
| Разраб. | _____ | | |
| Проверил | _____ | | |

Стадия У Лист 2 Листов 5