Вентиляция. Левый блок и расчетная ветвь С1

Аксонометрическая схема блока. М 1:100

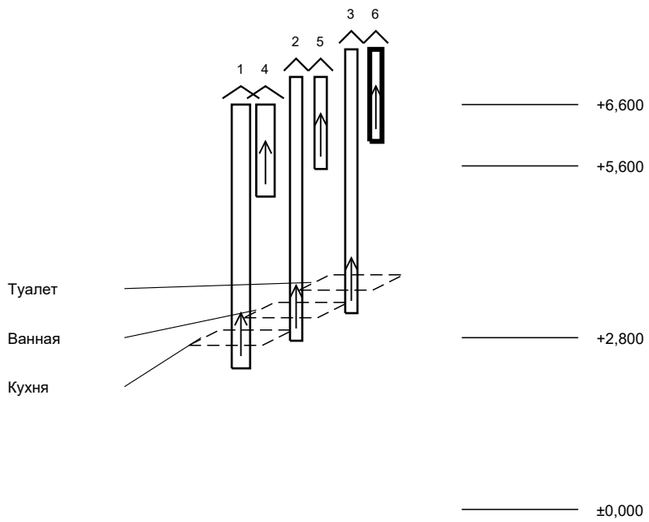

Расчетная ветвь С1. М 1:20

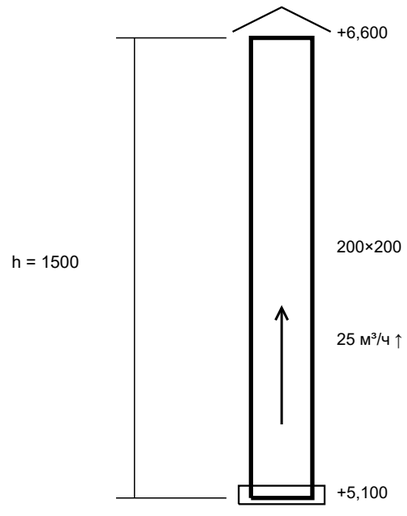

Выделенная ветвь: решетка туалета второго этажа → устье.

№	Канал	Этаж	L, м³/ч	Сечение, мм
1	К1	1	126	300×300
2	В1	1	25	200×200
3	С1	1	25	200×200
4	К1	2	126	300×300
5	В1	2	25	200×200
6	С1	2	25	200×200

К1: кухня 126 м³/ч; В1: ванная 25 м³/ч;

С1: туалет 25 м³/ч. Каждый канал — отдельный.

Решетки +2,300 / +5,100; устья +6,600 м.

Правый блок: К2 — 90 м³/ч, 250×250 мм;

В2 и С2 — по 25 м³/ч, 200×200 мм.

Расчетная ветвь С1 второго этажа:

h = 1,50 м; L = 25 м³/ч; 200×200 мм.

v = 0.17 м/с; ΔPe = 0.90 Па.

Потери = 0.07 Па; Σξ = 3,3.

Вход с решеткой ξ = 2; зонт ξ = 1,3.

Приток через неплотности принят по пособию.

Металлические каналы и их короба назначены по расчету; проходки на 50 мм шире сечения.

М 1:100

ОВ-178. Отопление и вентиляция здания

Вентиляция. Левый блок и расчетная ветвь С1

Жилой дом. Комсомольск-на-Амуре

	Фамилия	Подпись	Дата			
Разраб.	_____			Стадия У	Лист 5	Листов 5
Проверил	_____					