План подвала. Отопление

1:100

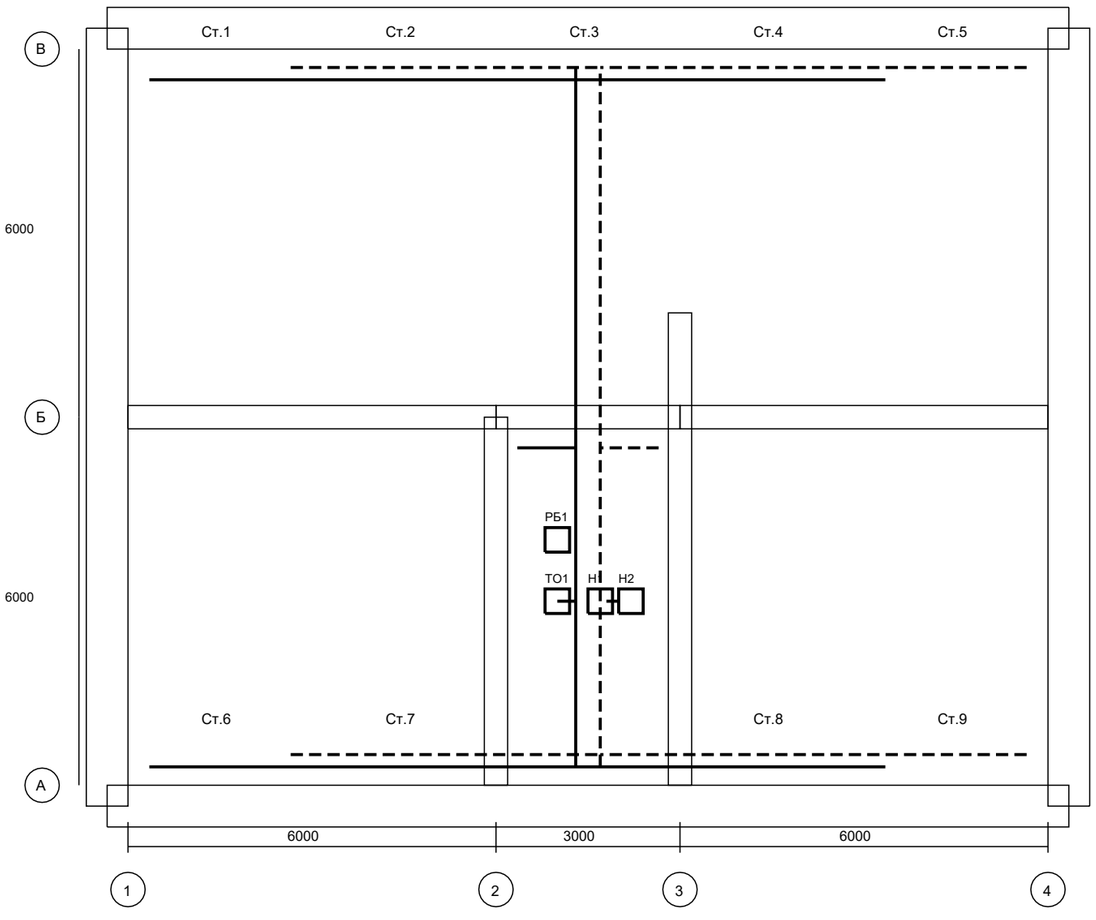

Фасад А–А — географический запад

Тепловой узел под лестничной клеткой.

Т1: DN25, ось −1,850 м.

Т2: DN25, ось −1,950 м.

Фасадные распределительные ветви DN20.

Стояки DN15; приборы подключены параллельно.

На основаниях стояков — запорная арматура и сливные краны; на ветвях — балансировка.

Горизонтальные трубы в подвале теплоизолировать.

Пол подвала −2,650 м; потолок −0,650 м.

Уклон 0,003 к точкам опорожнения принимается при деталировке; на компоновочном плане и в объемной модели уклон не развернут.

Размеры узла и места крепления условные.

Схема обвязки и обозначения — лист ОВ-4.

Насосы: один рабочий, один резервный.

Гибкие вставки и шумозащита узла — по монтажу.

ОВ-178 Отопление и вентиляция здания

Учебная РГР | Лист 1 | Масштаб 1:100