
План 1 этаж. Отопление и вертикаль

1:100

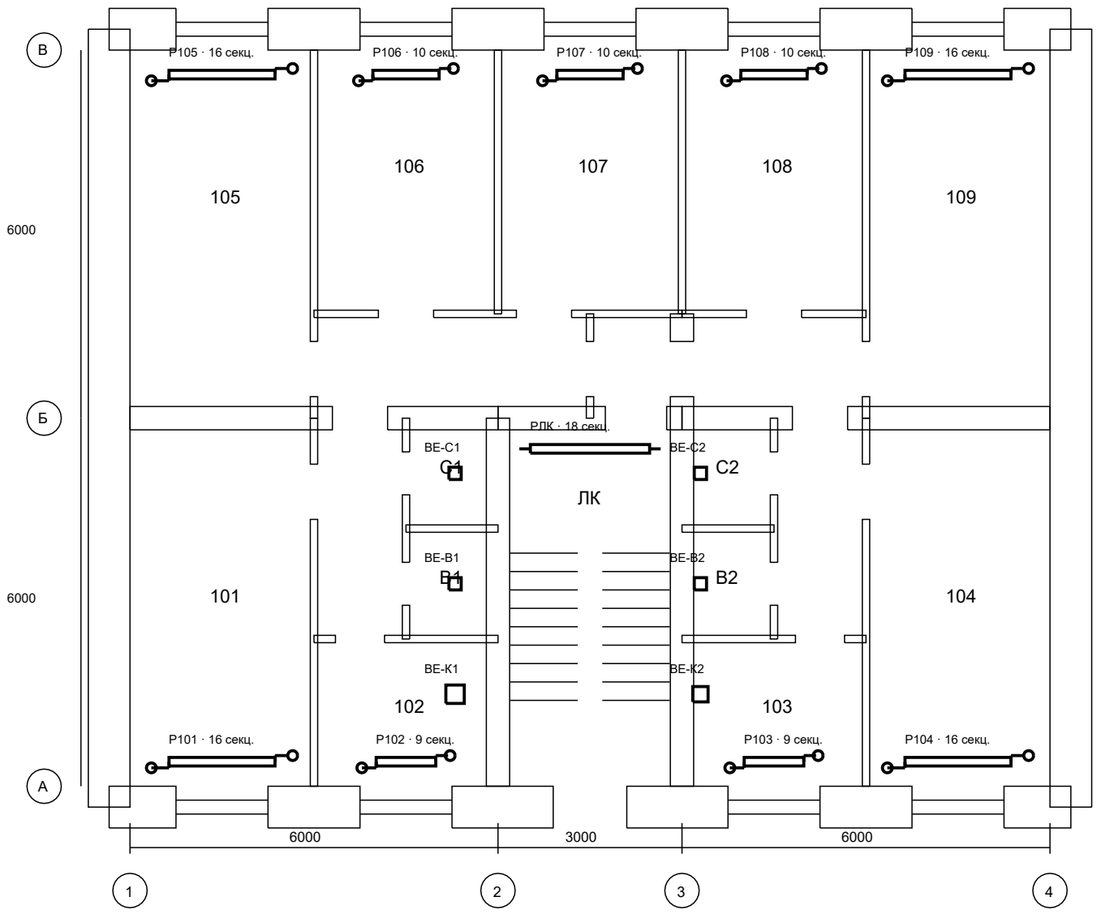

Фасад А–А — географический запад

Отопление: двухтрубное, нижняя разводка.

Внутренний график 85/60 °С.

Т1 — подача (сплошная); Т2 — обратка (штрих).

Стояки и подводки DN15.

МС-140-108; число секций указано у прибора.

На верхних приборах — краны Маевского.

На подводках — регулирующая и запорная арматура.

Вентиляция — раздельные естественные каналы.

К1: 126 м³/ч, 300×300 мм.

К2: 90 м³/ч, 250×250 мм.

В1/В2, С1/С2: по 25 м³/ч, 200×200 мм.

Приток — через неплотности ограждений

по учебной схеме пособия.

Переток — через дверные проемы.

Принятые размеры окон 1500×1400 мм;

подоконник 900 мм. Размеры и привязки

перегородок и лестницы восстановлены по плану.

Приборы шире окон размещены симметрично;

их габариты и проходы приняты компоновочно.

Арматура показана принципиально на схеме ОВ-4.

Конструкция венткоробов и изоляция не детализированы.

Работа вентиляции при герметичных окнах

данной учебной схемой не подтверждается.

Нагрузки помещений, Вт:

101: 1800 Вт; 16 секц.	102: 1080 Вт; 9 секц.
103: 1080 Вт; 9 секц.	104: 1800 Вт; 16 секц.
105: 1800 Вт; 16 секц.	106: 1080 Вт; 10 секц.
107: 1080 Вт; 10 секц.	108: 1080 Вт; 10 секц.
109: 1800 Вт; 16 секц.	ЛК: 2268 Вт; 18 секц.

ОВ-178 Отопление и вентиляция здания

Учебная РГР | Лист 2 | Масштаб 1:100