Расчетная аксонометрия отопления. Кольцо через Р105

Фрагмент: тепловой узел, магистрали, расчетный стояк 1

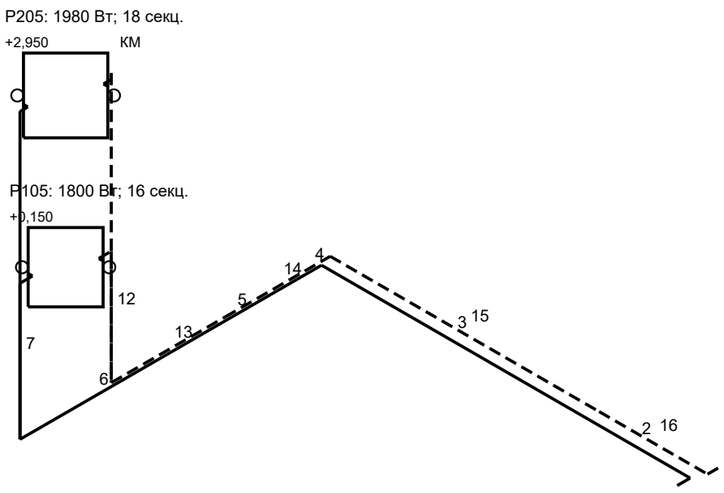

Т1 — сплошная линия, 85 °С.

Т2 — штриховая линия, 60 °С.

Обозначения участков соответствуют таблице расчета.

Короткие участки 1, 8–11, 17 — подводки и узел.

DN25 — магистрали; DN20 — распределение;

DN15 — стояки и подводки. КМ — кран Маевского.

Lкольца = 35.264 м; Σ(RL+Z) = 3190 Па.

На ветвях, не вошедших во фрагмент, — отводы к стоякам 2–10.

Запорная арматура и слив — у оснований стояков.

Увязка колец по пособию в РГР не выполняется.

Тепловой узел — принципиально, б/м

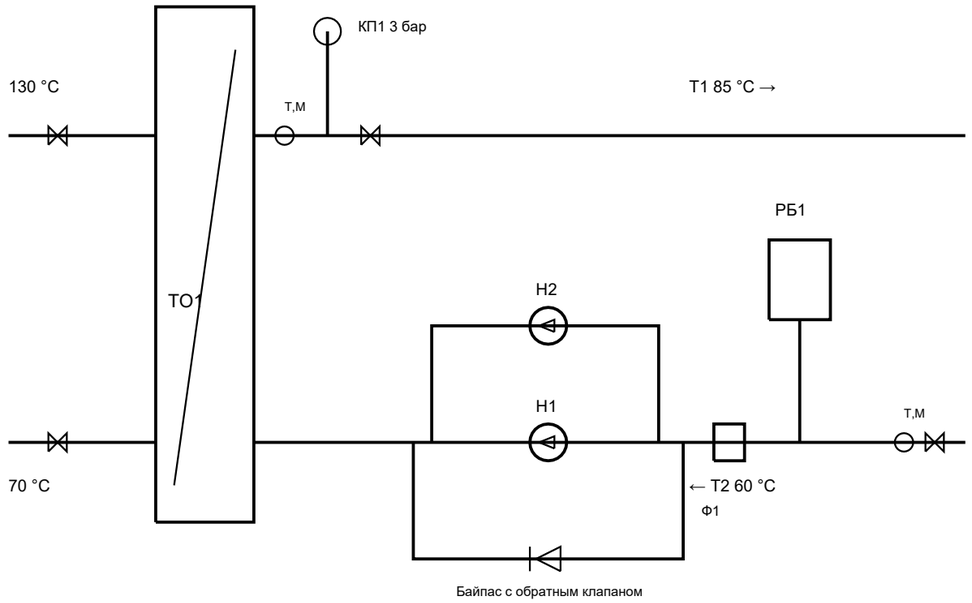

Н1, Н2: UPS 25-40; Q = 1.07 м³/ч; H = 1.1 м.

ТО1: СВ-51; расчетная поверхность не менее 0,20 м².

РБ1: мембранный бак 80 л; КП1: клапан 3 бар.

Ф1: фильтр. Т,М: термометр и манометр.

На входе первичного контура — регулирующий клапан.

Подпитка вторичного контура — через отдельный узел с защитой от обратного тока и контролем давления.

Подбор насоса — по полю Q–H пособия;

потери ТО1/Ф1 приняты 5/1 кПа, требуют уточнения.

Обвязка узла и габариты показаны условно.

Показанная схема не является монтажным узлом.

Уклоны и крепления на аксонометрии не развернуты.

ОВ-178 Отопление и вентиляция здания

Учебная РГР | Лист 4 | Масштаб 1:100